


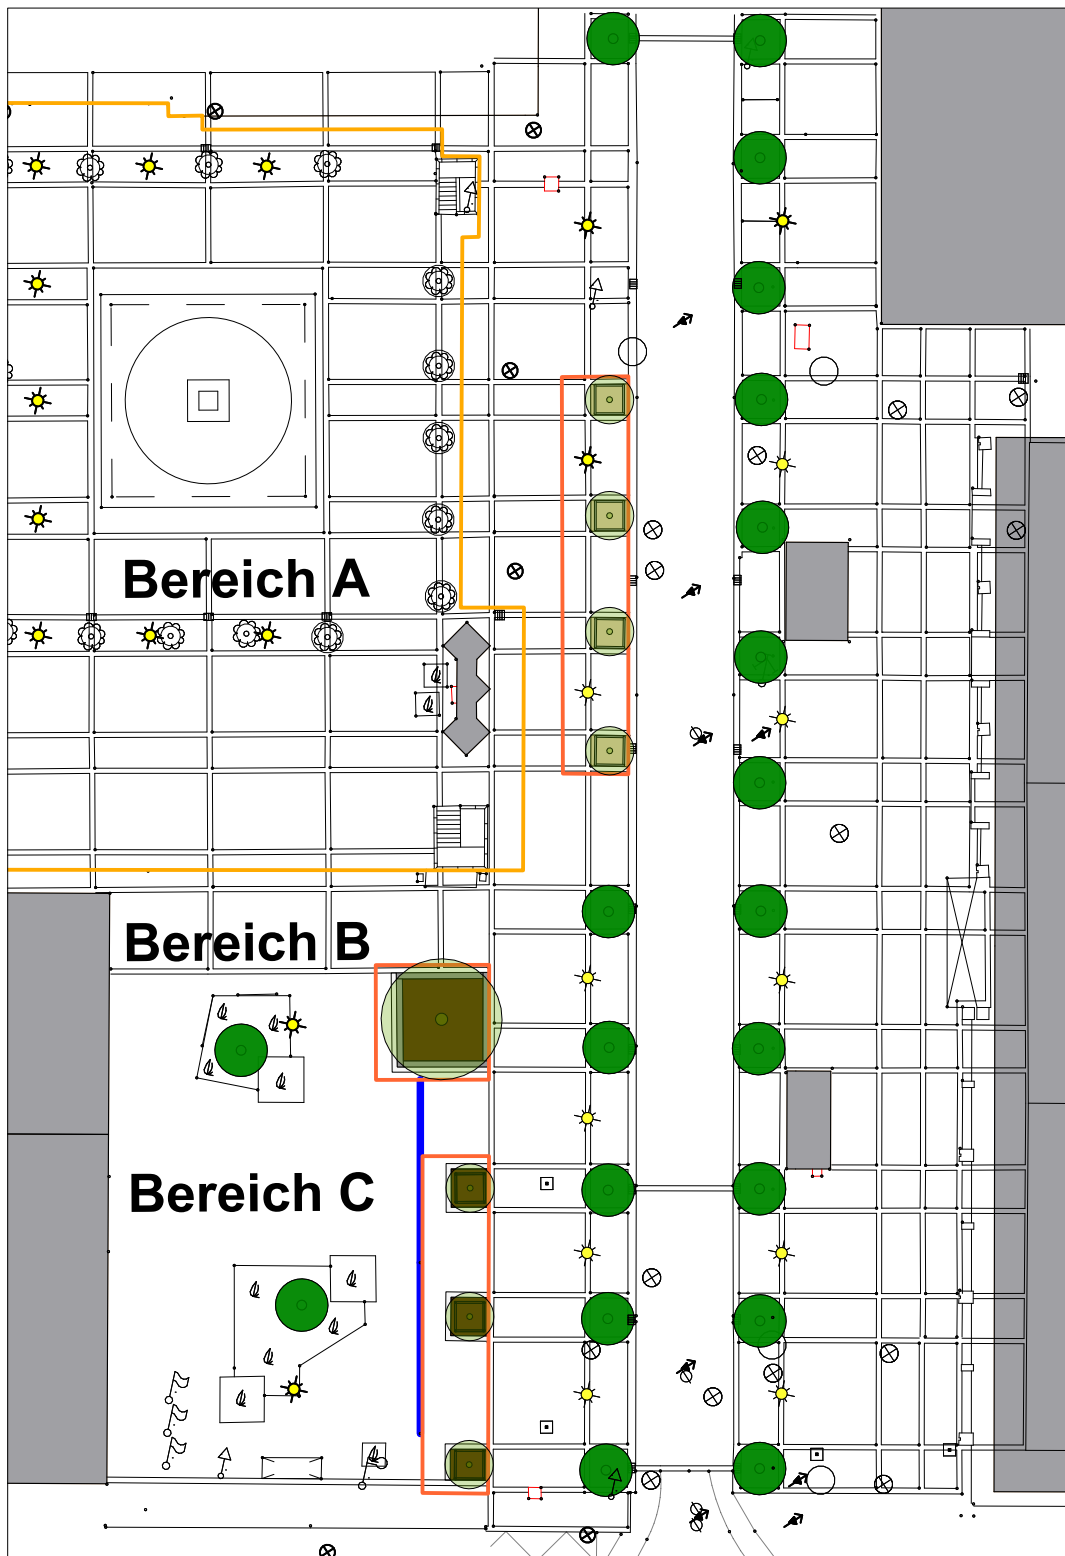

Legende

-  Bestandsbaum
-  Baumneupflanzung
-  Baumscheibe unterpflanzt
-  Baumscheibe Lava
-  OK Baugrube für Wurzelraumvergrößerung
-  Baumschutzring
-  Grenze Tiefgarage
-  Mastleuchte Bestand
-  Sitzblöcke Beton
-  Entwässerungsrinne
-  Granitzweizeiler

Stadt Erlangen

Abt. Stadtgrün



Fortführung Baumreihe Nürnberger Str. (FBNS)
- Vorentwurf -

Plan-Nr.1 Lageplan	Maßstab: 1:500 (DIN A4)	
Bearbeitung:	EB773-1 / Eilers	30.06.2021
Geändert:	1:500 (A4)	
SGL:	Rother	30.06.2021
Abt.-Ltg.:	Kintopp	30.06.2021

