


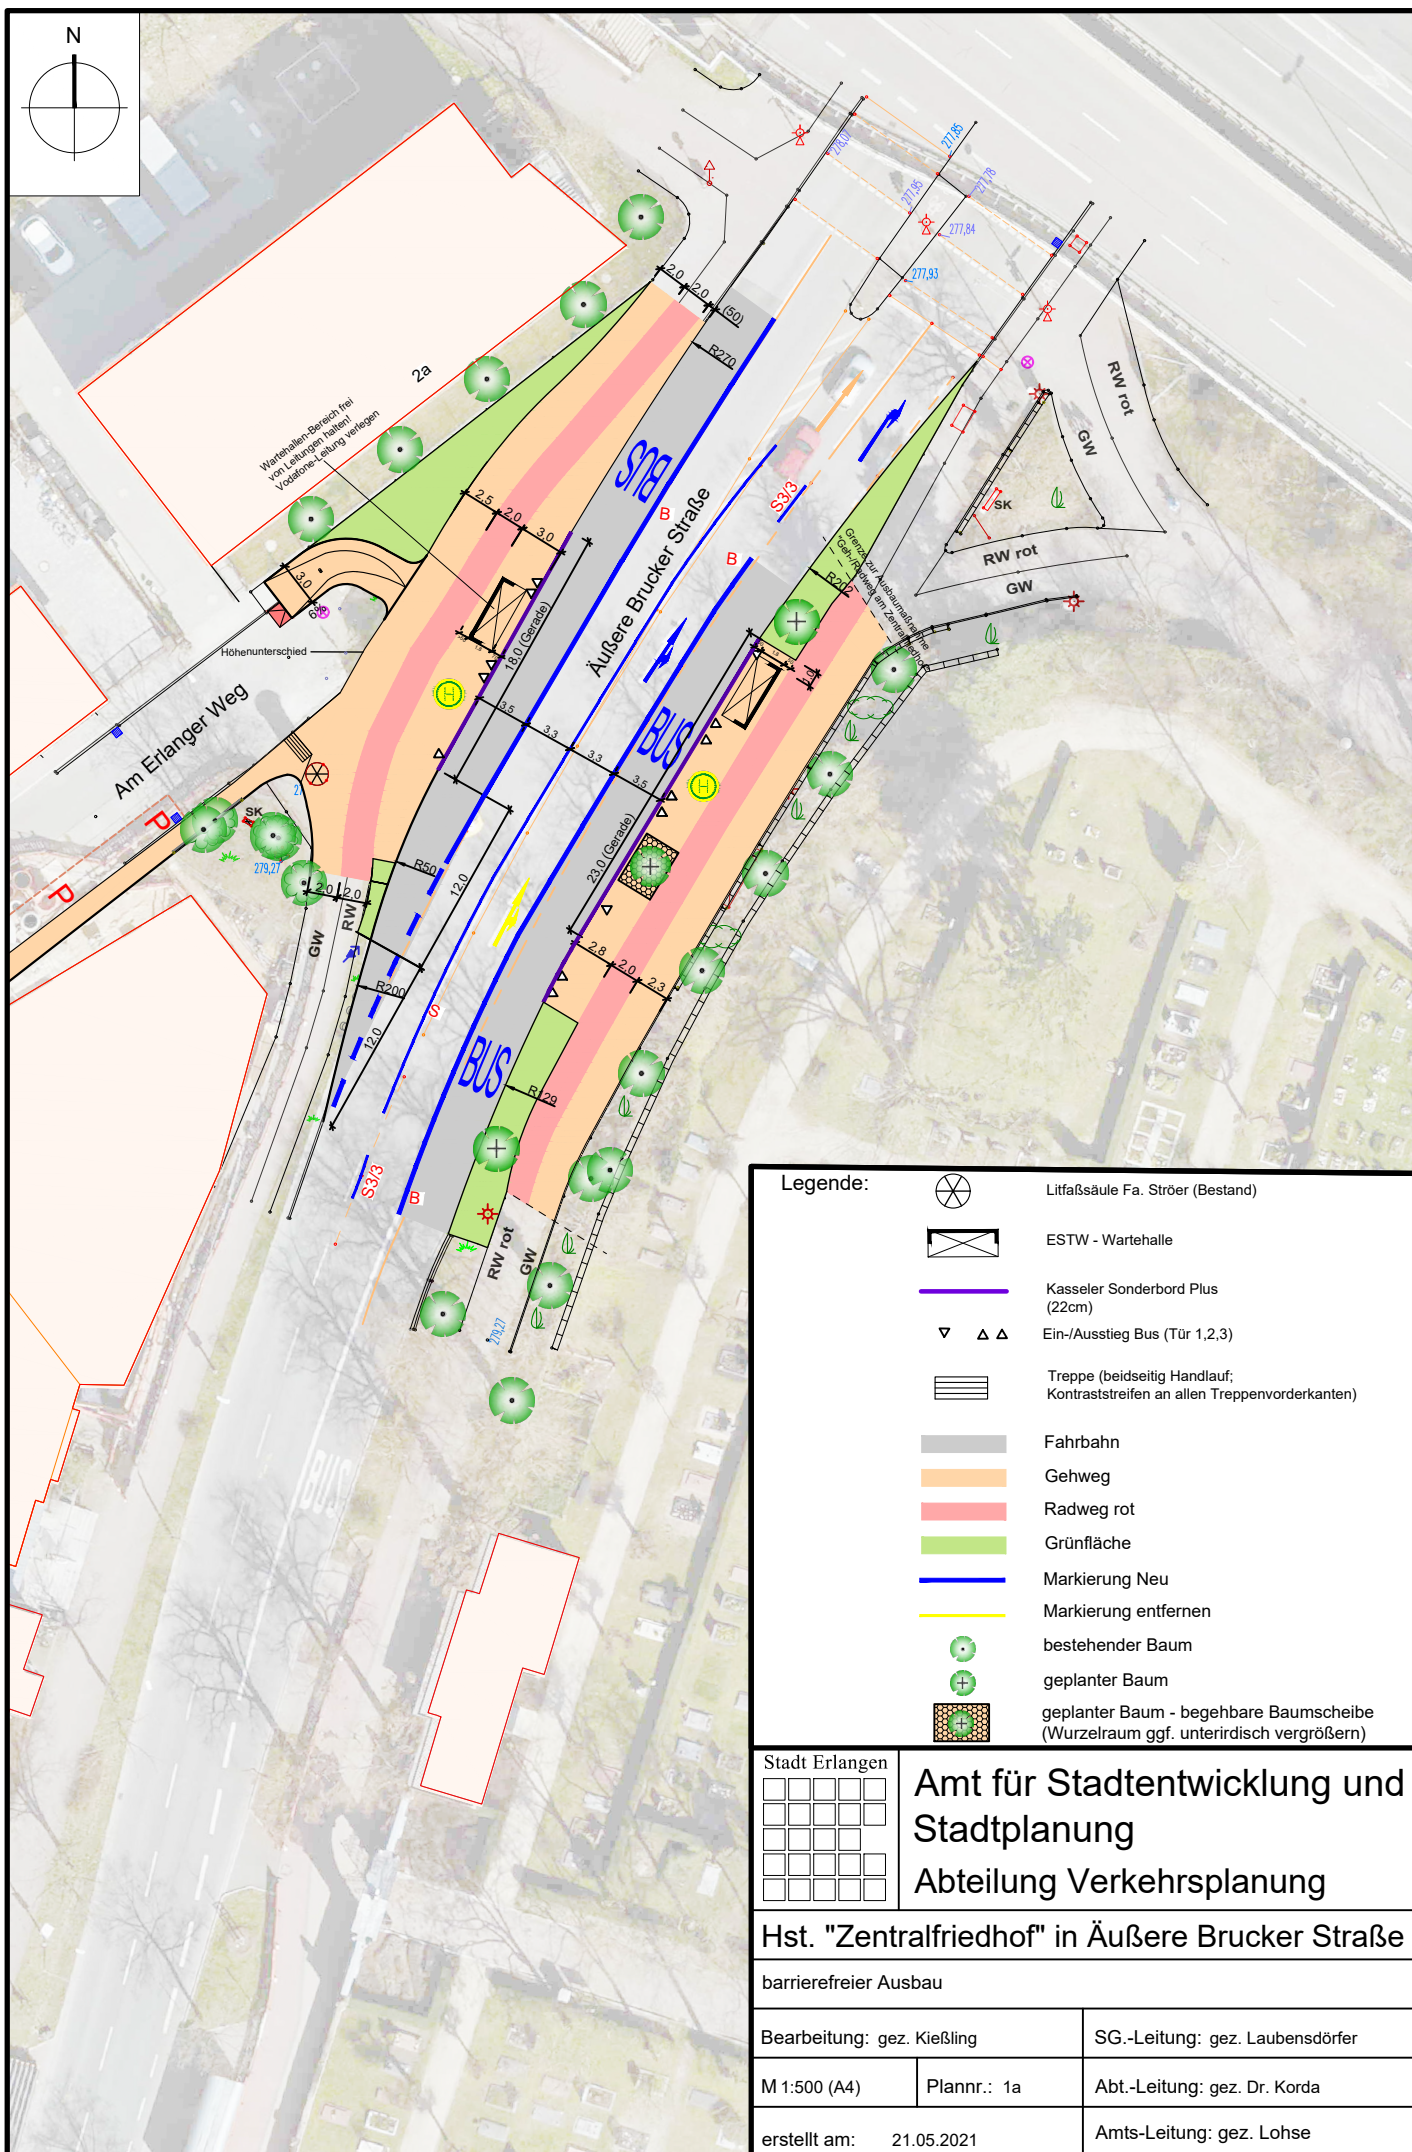

Legende:

- Litfaßsäule Fa. Ströer (Bestand)
- ESTW - Warthalle
- Kasseler Sonderbord Plus (22cm)
- Ein-/Ausstieg Bus (Tür 1,2,3)
- Treppe (beidseitig Handlauf; Kontraststreifen an allen Treppenvorderkanten)
- Fahrbahn
- Gehweg
- Radweg rot
- Grünfläche
- Markierung Neu
- Markierung entfernen
- bestehender Baum
- geplanter Baum
- geplanter Baum - begehbare Baumscheibe (Wurzelraum ggf. unterirdisch vergrößern)

Stadt Erlangen		Amt für Stadtentwicklung und Stadtplanung	
		Abteilung Verkehrsplanung	
Hst. "Zentralfriedhof" in Äußere Brucker Straße			
barrierefreier Ausbau			
Bearbeitung: gez. Kießling		SG.-Leitung: gez. Laubensdörfer	
M 1:500 (A4)	Plannr.: 1a	Abt.-Leitung: gez. Dr. Korda	
erstellt am: 21.05.2021		Amts-Leitung: gez. Lohse	