


Kleinräumige Trassenvarianten 1-8; Hutwiese Tennenlohe

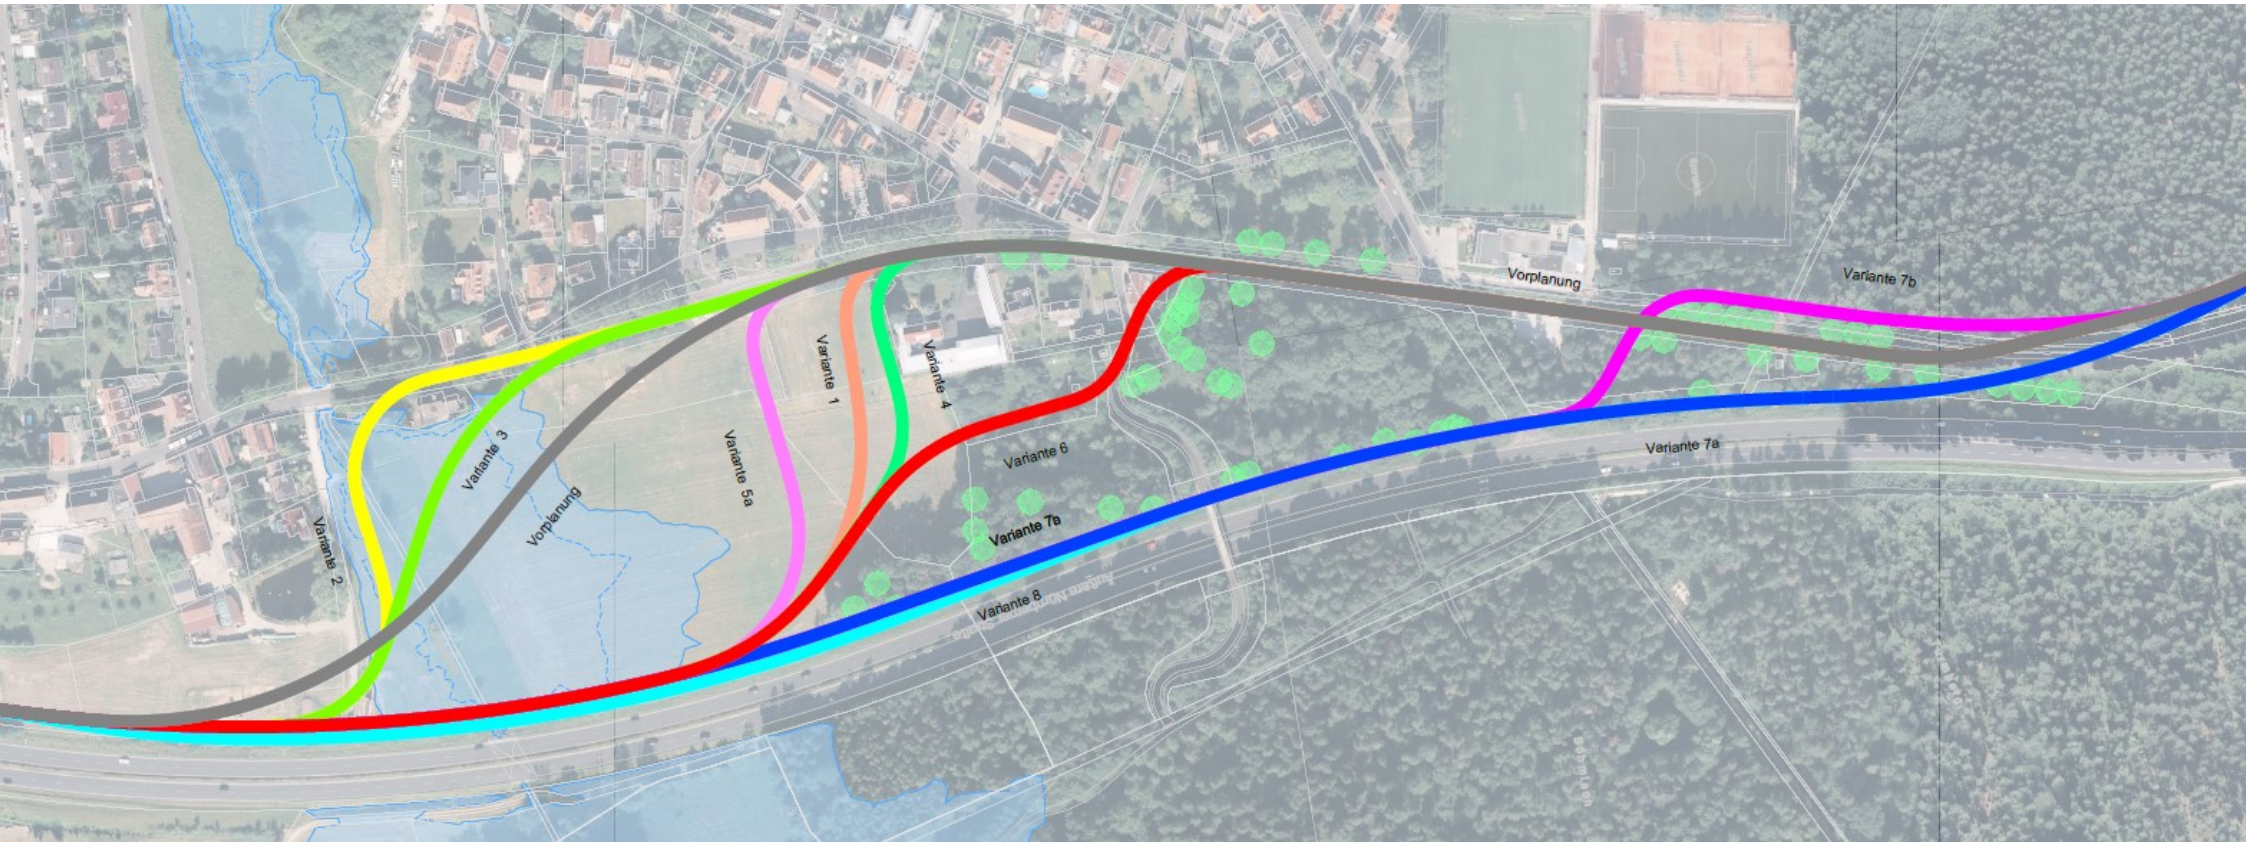

Vorlage VI/050/2021

Anlage 1

Kartendarstellung der Varianten 1-8

Bereich

Tennenlohe

Maßstab

-

Stand

16.02.2021

Planersteller

Ingenieurgemeinschaft StUB


Auszug aus Plan

T-G-005-2-SBT-171-LP-01000-1A



StUB
STADT-UMLAND-BAHN

Kleinräumige Trassenvariante 9; Hutwiese Tennenlohe

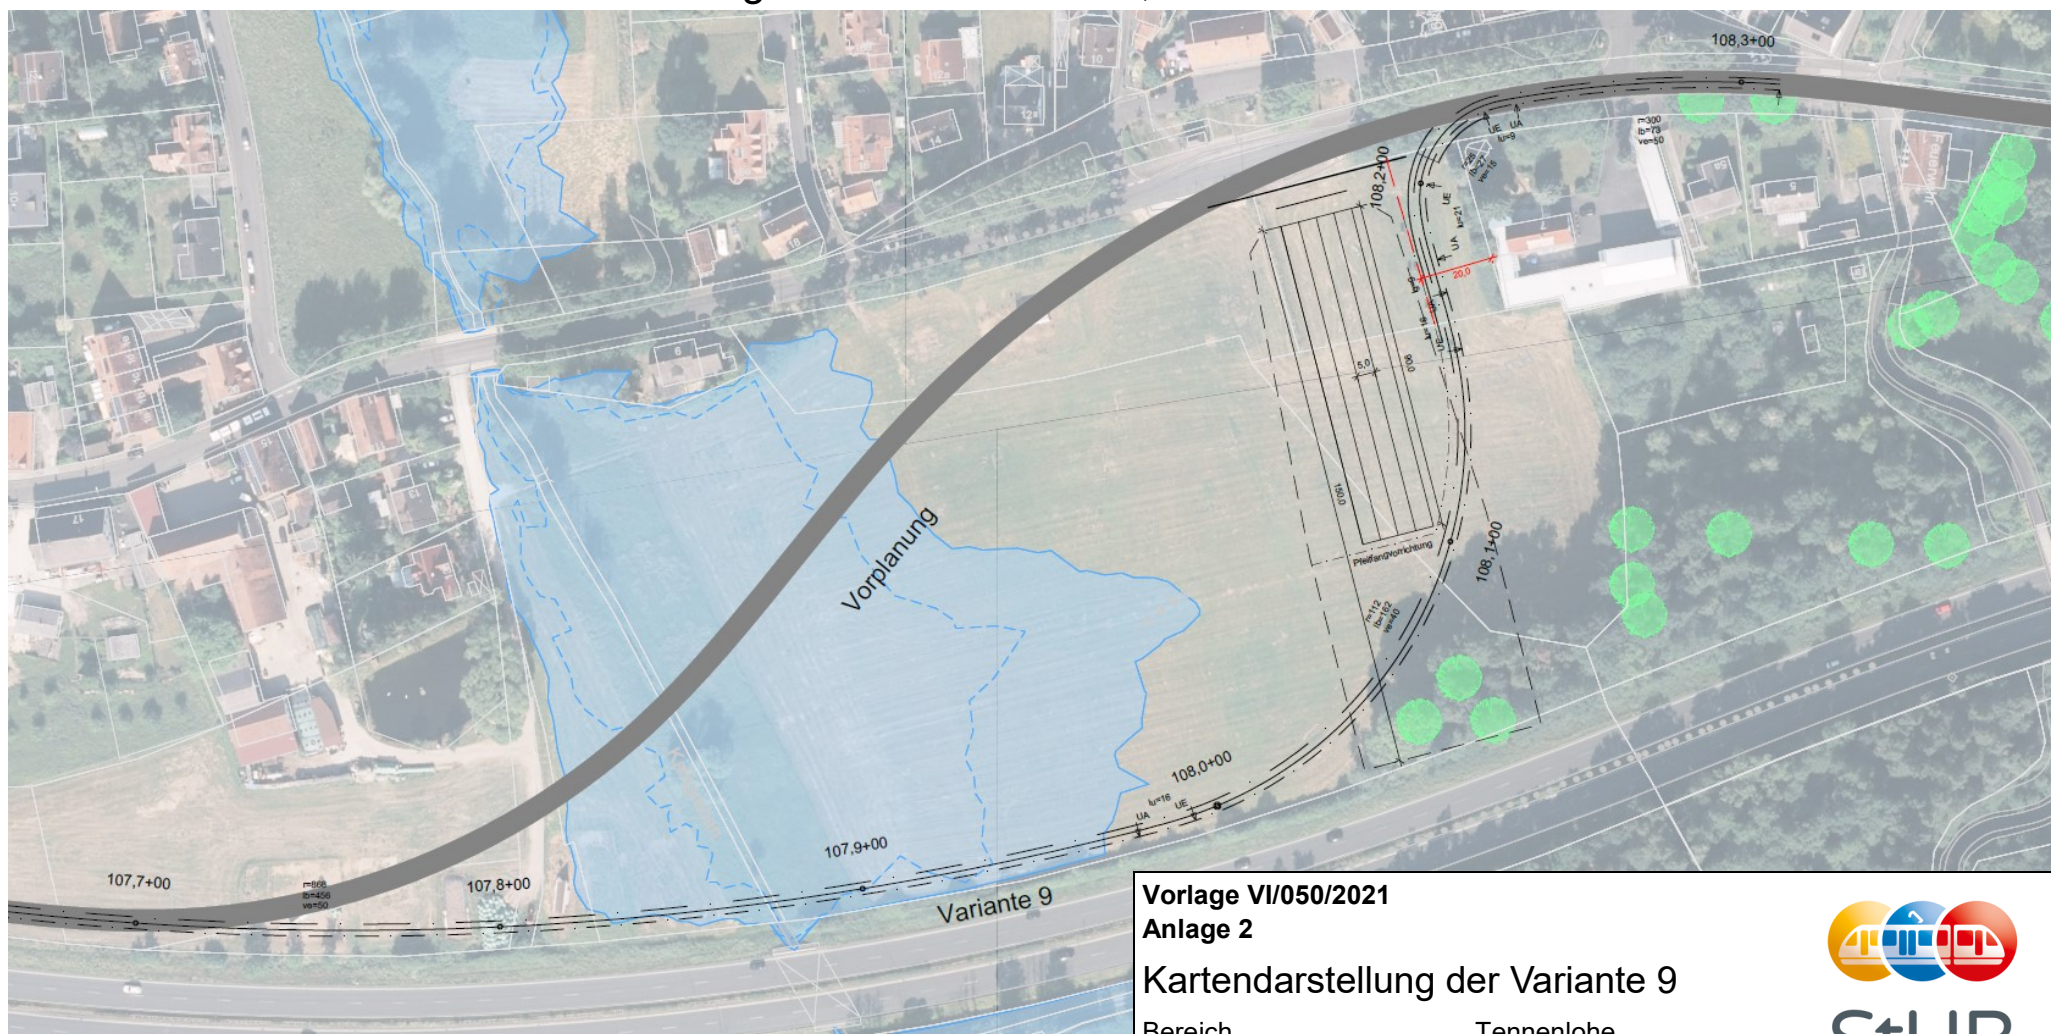

Vorlage VI/050/2021

Anlage 2

Kartendarstellung der Variante 9

Bereich

Tennenlohe

Maßstab

-

Stand

16.02.2021

Planersteller

Ingenieurgemeinschaft StUB

Auszug aus Plan

T-G-005-2-SBT-171-LP-01000-1A



StUB
STADT-UMLAND-BAHN

Ziel-gruppe	Kriterium	Beschreibung	Vorplanung - diagonal über Hutwiese		1 - Mitte Kirchweihplatz		2 - am Hutgraben auf Sebastianstraße		3 - diagonal über Hutgraben		4 - Kirchweihplatz Nord		5a (Weiterentwicklung von 5) - Kirchweihplatz Süd		6 - Feuerwehrhaus		7a - Bündelung B4		7b - Bündelung B4 mit kurzem Schwenk		8 - Bündelung näher an B4	
			Rang	Verbale Erläuterung	Rang	Verbale Erläuterung	Rang	Verbale Erläuterung	Rang	Verbale Erläuterung	Rang	Verbale Erläuterung	Rang	Verbale Erläuterung	Rang	Verbale Erläuterung	Rang	Verbale Erläuterung	Rang	Verbale Erläuterung	Rang	Verbale Erläuterung
Fahrgast	Fahrzeit	Dauer Durchfahrt	3/-	ca. 60 Sekunden Fahrzeitverlängerung gegenüber Variante 7a/8	4/-	circa 80 Sekunden Fahrzeitverlängerung gegenüber Variante 7a/8	4/-	circa 90 Sekunden Fahrzeitverlängerung gegenüber Variante 7a/8	3/--	vergleichbar mit Vorplanung; ca. 60 Sekunden Fahrzeitverlängerung gegenüber Variante 7a/8	4/-	circa 80 Sekunden Fahrzeitverlängerung gegenüber Variante 7a/8	4/-	circa 90 Sekunden Fahrzeitverlängerung gegenüber Variante 7a/8	4/-	circa 90 Sekunden Fahrzeitverlängerung gegenüber Variante 7a/8	1	beste Fahrzeit	2/-	circa 30 Sekunden mehr Fahrzeit	1	beste Fahrzeit
	Lage	Einsehbarkeit Haltestelle Verknüpfung Haltestelle mit weiterem ÖPNV Zugang zur Haltestelle	1	Haltestelle auf Fahrbahn, gut einsehbar, Verknüpfung zu Bushaltestelle Skulpturenpark für Umstiege, gute Erschließung	1	Haltestelle auf Fahrbahn, gut einsehbar, Verknüpfung zu Bushaltestelle Skulpturenpark für Umstiege, gute Erschließung	1	Haltestelle auf Fahrbahn, gut einsehbar, Verknüpfung zu Bushaltestelle Skulpturenpark für Umstiege, gute Erschließung	1	Haltestelle auf Fahrbahn, gut einsehbar, Verknüpfung zu Bushaltestelle Skulpturenpark für Umstiege, gute Erschließung	1	Haltestelle auf Fahrbahn, gut einsehbar, Verknüpfung zu Bushaltestelle Skulpturenpark für Umstiege, gute Erschließung	1	Haltestelle auf Fahrbahn, gut einsehbar, Verknüpfung zu Bushaltestelle Skulpturenpark für Umstiege, gute Erschließung	1	Haltestelle auf Fahrbahn, gut einsehbar, Verknüpfung zu Bushaltestelle Skulpturenpark für Umstiege, gute Erschließung	2/--	schlechte Einsehbarkeit der Haltestelle Verknüpfung zu weiteren Buslinien und Erschließung nur durch lange Zuwegung	2/--	schlechte Einsehbarkeit der Haltestelle Verknüpfung zu weiteren Buslinien und Erschließung nur durch lange Zuwegung	2/--	schlechte Einsehbarkeit der Haltestelle Verknüpfung zu weiteren Buslinien und Erschließung nur durch lange Zuwegung
Betrieb		Störungsanfälligkeit Streckenführung (Radien) Länge des Bahnkörpers / der Bahnkörper	3	große Bögen, ca. 50 % straßenbündig, Störungsanfälligkeit im Bereich Kreuzung der Straße und Befahren der Straße Abschnittslänge circa 1340 m	4	enger Radius bei Einfahrt in Sebastianstraße leicht geringerer straßenbündiger Abschnitt	5	enge Radien, maximale Länge straßenbündig	4	länger straßenbündig aber große Bogenradien	4	enger Radius bei Einfahrt in Sebastianstraße leicht geringerer straßenbündiger Abschnitt Abschnitt circa 60 m länger	4/-	zwei enge Radien Länge des straßenbündigen Bahnkörpers circa wie Vorplanung Abschnitt circa 80 m länger	3	zwei enge Radien mehrerheitlich unabhängiger Bahnkörper Abschnitt circa 10 m kürzer	1	optimale Streckenführung, keine engen Radien, potentielle Beeinträchtigung lediglich an BÜ Sebastianstraße unabhängiger BK Abschnitt circa 70 m kürzer	2/-	2 enge Radien am BÜ Sebastianstraße; nur unabhängiger Bahnkörper Abschnitt circa 50 m kürzer	1	optimale Streckenführung, keine engen Radien, potentielle Beeinträchtigung lediglich an BÜ Sebastianstraße unabhängiger BK Abschnitt circa 70 m kürzer
Kommune	Kosten	Investitionen	1	ca. 4,9 Mio. EUR	2	ca. 5,4 Mio. EUR	2	ca. 5,4 Mio. EUR	2	ca. 5,3 Mio. EUR	2	ca. 5,4 Mio. EUR	2	ca. 5,5 Mio. EUR	4	ca. 7,6 Mio. EUR (inkl. 2 Mio Neubau Gerätehaus)	3	ca. 5,8 Mio. EUR	3	ca. 5,8 Mio. EUR	3	ca. 5,8 Mio. EUR
	Konflikte Individualverkehr	Schnittstellen	3	Einfädelerung auf Straße in Höhe Kirche und nach Feldweg zu Walderlebniszentrum, Schaffung von zwei LSA/Kreuzungen StÜB/MIV	3/-	Einfädelerung in die Sebastianstraße in engem Bogen, längere Ampelphase, Schaffung von zwei LSA/Kreuzungen StÜB/MIV	4	Einfädelerung in die Sebastianstraße in engem Bogen, längere Ampelphase, Schaffung von zwei LSA/Kreuzungen StÜB/MIV längster straßenbündiger Bereich mit weiteren Einmündungen	3	Einfädelerung auf Straße in Höhe Kirche und nach Feldweg zu Walderlebniszentrum, Schaffung von zwei LSA/Kreuzungen StÜB/MIV	3/-	Einfädelerung in die Sebastianstraße in engem Bogen, längere Ampelphase Schaffung von zwei LSA/Kreuzungen StÜB/MIV	3	Einfädelerung in die Sebastianstraße in engem Bogen, längere Ampelphase Schaffung von zwei LSA/Kreuzungen StÜB/MIV	3	Einfädelerung auf Straße in Höhe Ausfahrt Feuerwehr Schaffung von zwei LSA / Kreuzungen StÜB / MIV Einfädelerung in die Sebastianstraße in engem Bogen	1	Kreuzung in flachem Winkel der Sebastianstraße, dadurch schnelle Räumzeit des BÜ durch StÜB	2	Kreuzung in steilem Winkel, dadurch hohe Räumzeit der StÜB	1	Kreuzung in flachem Winkel der Sebastianstraße, dadurch schnelle Räumzeit des BÜ durch StÜB
	Konflikte Landwirtschaft	Konfliktpunkte mit landwirtschaftlicher Aktivität durch Flächenverlust und eingeschränkte Zufahrtsmöglichkeiten	2/---	starke Zerschneidung landwirtschaftlich genutzter Flächen	1	landwirtschaftliche Flächen nur randseitig betroffen	1	landwirtschaftliche Flächen nur randseitig betroffen	2/---	starke Zerschneidung landwirtschaftlich genutzter Flächen	1	landwirtschaftliche Flächen nur randseitig betroffen	1	landwirtschaftliche Flächen nur randseitig betroffen	1	landwirtschaftliche Flächen nur randseitig betroffen	2	landwirtschaftliche Flächen nur randseitig betroffen, forstwirtschaftliche Flächen betroffen	2	landwirtschaftliche Flächen nur randseitig betroffen, forstwirtschaftliche Flächen betroffen	2/+	landwirtschaftliche Flächen nur randseitig betroffen, forstwirtschaftliche Flächen gegenüber 7a optimiert aber weiterhin betroffen
	Sonstige Konflikte	bestehende Nutzungen / Gebäude; Freizeitnutzung: Beeinträchtigung Schützenverein / Kirchweihplatz	1	keine Inanspruchnahme Kirchweihgelände sowie Bogenschießplatz	3	mittige Inanspruchnahme Kirchweihgelände sowie Bogenschießplatz	3	keine Inanspruchnahme Kirchweihgelände sowie Bogenschießplatz; Baugrundstück betroffen	1	keine Inanspruchnahme Kirchweihgelände sowie Bogenschießplatz	3	teilweise Inanspruchnahme Kirchweihgelände sowie Bogenschießplatz; Ecke Privatgrund (Baugrundstück) betroffen	2	keine Inanspruchnahme Kirchweihgelände; Bogenschießplatz randseitig betroffen	4	keine Inanspruchnahme Kirchweihgelände; Bogenschießplatz randseitig betroffen; aber privates Gartengrundstück und Feuerwehrhaus	1	keine Inanspruchnahme Kirchweihgelände sowie Bogenschießplatz	1	keine Inanspruchnahme Kirchweihgelände sowie Bogenschießplatz	1	keine Inanspruchnahme Kirchweihgelände sowie Bogenschießplatz
Allgemeinheit	Strecken-sensitivität	Eingriff in Hutgraben, sofern nicht bei "Umwelt und Natur" abgebildet	3	diagonal durch Hochwassergefahrenfläche	1	randseitig durch Hochwassergefahrenfläche, "HQ häufig" kaum beeinflusst	2	längs durch Hochwassergefahrenfläche	3	diagonal durch Hochwassergefahrenfläche	1	randseitig durch Hochwassergefahrenfläche, "HQ häufig" kaum beeinflusst	1	randseitig durch Hochwassergefahrenfläche, "HQ häufig" kaum beeinflusst	1	randseitig durch Hochwassergefahrenfläche, "HQ häufig" kaum beeinflusst	1	randseitig durch Hochwassergefahrenfläche, "HQ häufig" kaum beeinflusst	1	randseitig durch Hochwassergefahrenfläche, "HQ häufig" kaum beeinflusst	1	randseitig durch Hochwassergefahrenfläche, "HQ häufig" kaum beeinflusst
	Schall / Erschütterungen	Betroffenheit Anlieger	3	Sebastianstr. bis Nr. 8 betroffen; An der Wied	3	Sebastianstr. bis Nr. 8 betroffen; An der Wied	6	stärkste Betroffenheit bis Nr. 13a/18; An der Wied	5	Sebastianstr. bis Nr. 18 betroffen - Nr. 9 stark betroffen; An der Wied	4	Sebastianstr. bis Nr. 8 betroffen - Nr. 7 stark betroffen; An der Wied	3	Sebastianstr. bis Nr. 8 betroffen; An der Wied	2	Sebastianstr. 5-7 rückseitig betroffen; An der Wied	1	großer Abstand zu Bebauung	1	großer Abstand zu Bebauung	1	großer Abstand zu Bebauung
	Baubedingte Auswirkungen	Konfliktpotenzial mit Nutzungen im Baubereich / Komplexität der Bauabwicklung Länge des betroffenen Bereiches	3	bauzeitliche Einschränkungen des Individualverkehrs, Maßnahmen für Anfahrt Feuerwehr erforderlich ca. 1,3 km Länge	1	bauzeitliche Einschränkungen des Individualverkehrs, Maßnahmen für Anfahrt Feuerwehr erforderlich bündig mit B4 einfacher zu realisieren	3	bauzeitliche Einschränkungen des Individualverkehrs, Maßnahmen für Anfahrt Feuerwehr erforderlich länger als Vorplanung	3	bauzeitliche Einschränkungen des Individualverkehrs, Maßnahmen für Anfahrt Feuerwehr erforderlich länger als Vorplanung	1	bauzeitliche Einschränkungen des Individualverkehrs, Maßnahmen für Anfahrt Feuerwehr erforderlich Querung des Retentionsraumes bündig mit B4 einfacher zu realisieren	1	bauzeitliche Einschränkungen des Individualverkehrs, Maßnahmen für Anfahrt Feuerwehr erforderlich Querung des Retentionsraumes bündig mit B4 einfacher zu realisieren	1/-	bauzeitlich geringere Einschränkungen des Individualverkehrs, keine Beeinträchtigung der Feuerwehr (Voraussetzung: Gerätehaus bereits an neuem Standort) Umverlegung der Rad-/Gehwegrampe über B4 zu Reichswald Querung des Retentionsraumes bündig mit B4 einfacher zu realisieren	2	bauzeitlich kaum Einschränkungen für MIV, Feuerwehr und Landwirtschaft massive Einschränkung durch Neubau der Brücke über B4 sowie Neubau des Rampenbauwerks circa 70 m kürzer Querung des Retentionsraumes bündig mit B4 einfacher zu realisieren	2	bauzeitlich kaum Einschränkungen für MIV, Feuerwehr und Landwirtschaft massive Einschränkung durch Neubau der Brücke über B4 sowie Neubau des Rampenbauwerks circa 50 m kürzer Querung des Retentionsraumes bündig mit B4 einfacher zu realisieren	2	bauzeitlich kaum Einschränkungen für MIV, Feuerwehr und Landwirtschaft massive Einschränkung durch Neubau der Brücke über B4 sowie Neubau des Rampenbauwerks circa 70 m kürzer Querung des Retentionsraumes bündig mit B4 einfacher zu realisieren
Natur und Umwelt	Schutzgüter der Umwelt	Schutzgüter gemäß UVPG	1/-		2		3		3		2		1		4		6		5		6	
	Artenschutz	Lebensraumverlust bzw. Störung geschützter Arten	1/+++		1/+++		1/+++		1/+++		1/+++		1/+++		2/+++		4		3/+		4	
	Natura 2000	Verlust von Höhlenbäumen im Kernhabitat	1/+++		1/+++		1/+++		1/+++		1/+++		1/+++		2/+++	1 schützenswerter Baumstandort	3	Innerhalb des Trassenverlaufs sind 8 schützenswerte Baumstandorte verzeichnet	3	Innerhalb des Trassenverlaufs sind 8 schützenswerte Baumstandorte verzeichnet größere "Schneise" aufgrund der Bögen zur Querung der Sebastianstraße	3	Innerhalb des Trassenverlaufs sind 8 schützenswerte Baumstandorte verzeichnet
	Wasser (WRRL)	Bewertung gemäß der europäischen Wasserrahmenrichtlinie	1		1		1/-	Aufgrund des nahezu parallelen Verlaufs zum Hutgraben, stärkere Eingriffe nicht auszuschließen	1		1		1		1		1		1		1	
Gesamtwertung		Die Bewertung im Bereich Natur und Umwelt ist bei betroffenen Verbots-tatbeständen maßgeblich für die Gesamtwertung					Trassenoptimierung in Richtung Var. 4 ohne Eingriff Privatgrund denkbar		im Vergleich keine entscheidenden Vorteile erkennbar; daher nicht weiterverfolgen			nicht umsetzbar, da Eingriff in Privatgrund schwer zu rechtfertigen (Var. 1, 5a liegen alternativ vor)			nicht umsetzbar, da Ersatzneubau Feuerwehr in Folge StÜB unrealistisch und in Abwägung nicht wirtschaftlich. Zudem Eingriffe in Privatgrund und Baumbestand.		Aus Bewertungsergebnis Umwelt nicht umsetzbar; daher nicht weiterverfolgen		Aus Bewertungsergebnis Umwelt nicht umsetzbar; daher nicht weiterverfolgen		Aus Bewertungsergebnis Umwelt nicht umsetzbar; daher nicht weiterverfolgen	

Die Rangfolge wird je Zeile im Vergleich der Varianten gebildet; dieses Vorgehen lehnt sich an die Vorgehensweise nach UVPG ab. Es bildet zeilenweise die relative Rangfolge von der - in diesem Kriterium - besten (1) hin zur schlechtesten Variante (höchster Zahlenwert) ab.

Stand: 13.01.2021 12:00 - Gräf
16.10.2020 Erstaussgabe
23.10.2020 redaktionelle Überarbeitung
13.01.2021 Var. 1 Gesamtwertung erläutert, Var. 4 wegen Eingriff Privatgrund (Wohnbaufläche) abgewertet, Var. 6 Gesamtwertung ausgebaut
19.01.2021 Gesamtwertung Var. 4 und 6 redaktionell angepasst

Gutachterliche Empfehlung
Rangfolge der Varianten: 1 – bessere Variante, 2 – nachrangige Variante
+ leichter Vorteil, ++ deutlicher Vorteil, +++ sehr deutlicher Vorteil, ⇔ gleichrangig
Fett: Vorteil in Auswirkungsklasse I
Rot umrandet: Notwendigkeit einer artenschutzrechtliche Ausnahme oder einer Abweichung vom Schutzregime Natura 2000 erfordert die Wahl der günstigeren zumutbaren Alternative (§45 Abs. 7 BNatSchG bzw. §34 Abs. 3 Nr. 2 BNatSchG)

Höchste betroffene Auswirkungsklasse (vgl. Kap. 1.4.2):

I
II
III