


Anlage 3

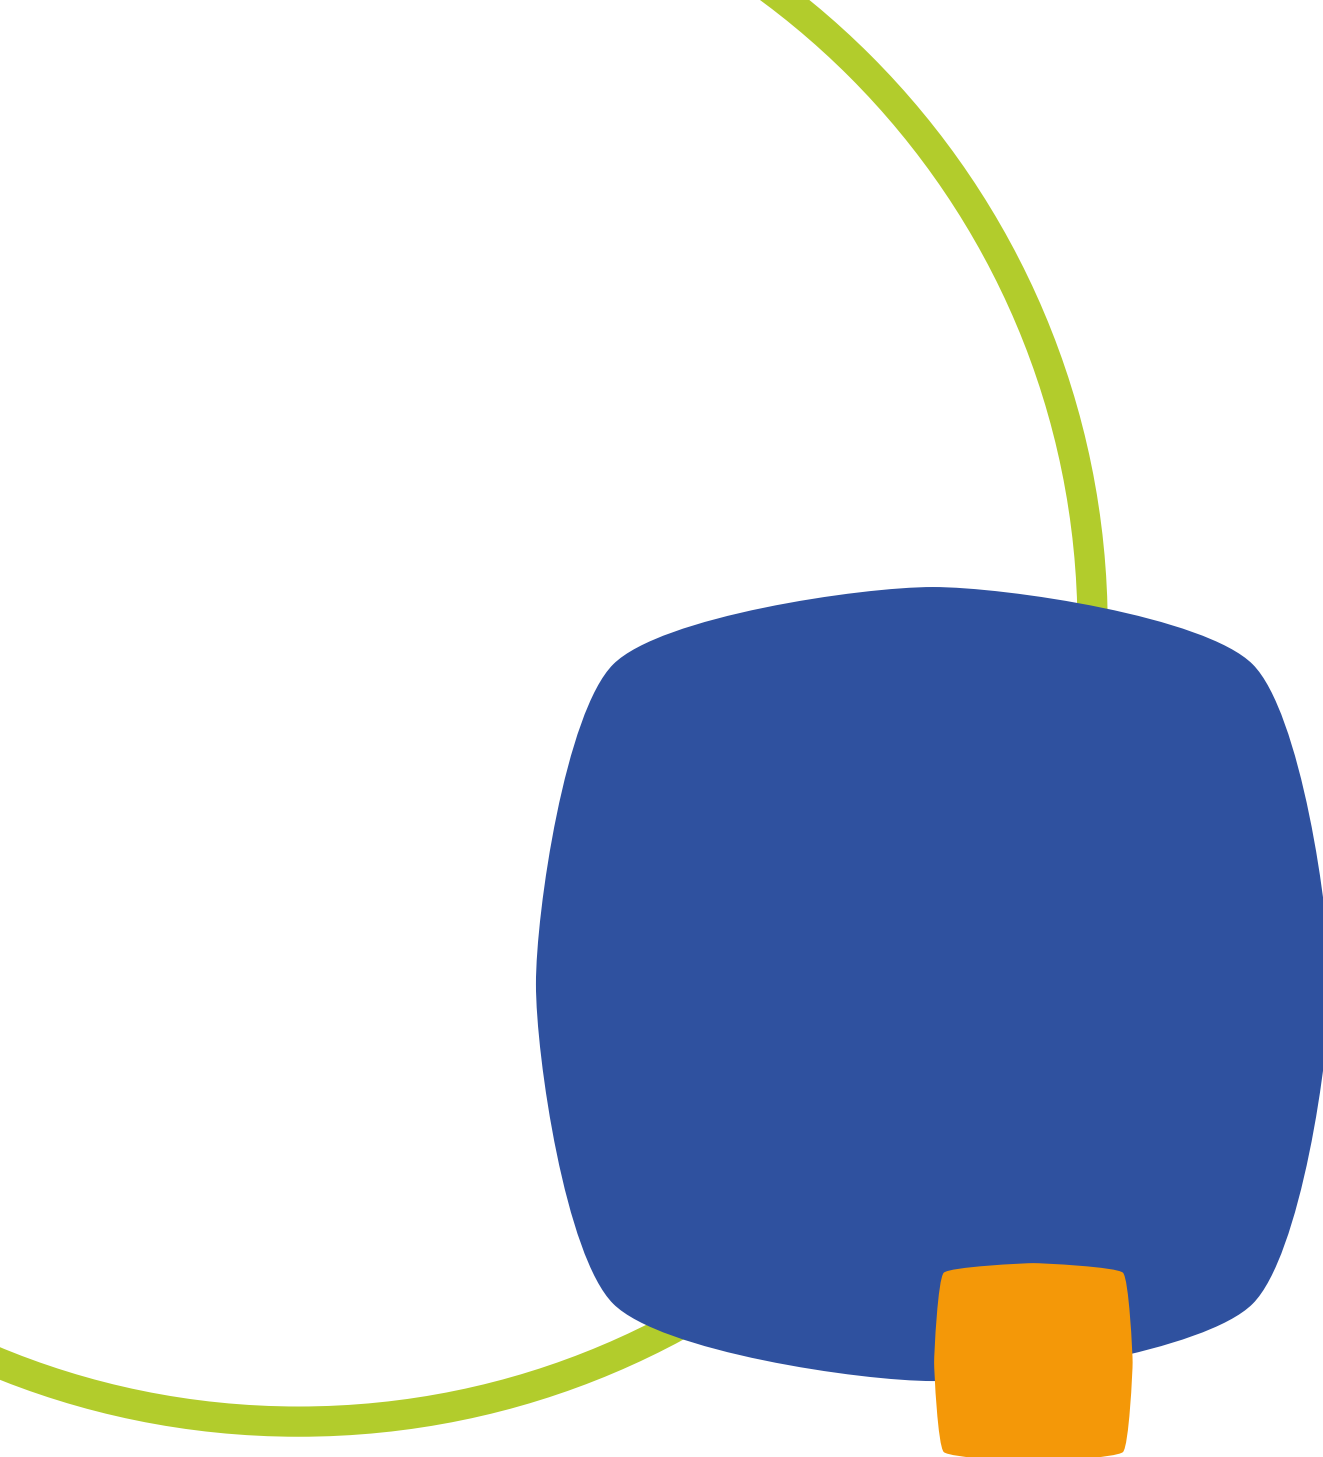


Erläuterungsbericht

Neugestaltung Egidienplatz


Umgestaltung Egidienplatz - Variante 1

ursprüngliche Planung mit Aufstellfläche Autoscooter

 

Planzeichnung: adlerolesch LANDSCHAFTSARCHITEKTEN GmbH

Umgestaltung Egidienplatz - Variante 2

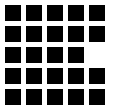

Umplanung ohne Aufstellfläche Autoscooter



Planzeichnung: adlerolesch LANDSCHAFTSARCHITEKTEN GmbH

Egidienplatz Erlangen

Umgestaltung Verkehrsanlagen

BAUHERR:

Stadt Erlangen vertreten durch das Amt für
Stadtplanung und Mobilität
Gebbertstraße 1
91052 Erlangen

LANDSCHAFTSARCHITEKT:

adlerolesch LANDSCHAFTSARCHITEKTEN GmbH
Marienstraße 8
90402 Nürnberg

ERLÄUTERUNGSBERICHT
VORENTWURF
VERKEHRSANLAGEN

Nürnberg, 02.08.2023

INHALT

1. Lage und heutige Situation.....	3
2. Verkehrliche Einbindung	3
3. Abwägung Kreisverkehr oder T-Kreuzung.....	3
4. Besondere Anforderung Kerwa	4
5. Variantenuntersuchung Verkehrsknotenpunkt Vertiefung (Oktober 2022)	4
6. Gehölzbestand, Neupflanzung und Grünflächen.....	5
7. Renaturierung des Eltersdorfer Baches / Überflutung	5
8. Materialkonzept: Einbauten und Ausstattung.....	5
9. Materialkonzept: Oberflächen	6

ANLAGEN

A Lageplan Vorentwurf

- 2.01-B - Variante mit Autoscooter
- 2.10-A - Variante ohne Autoscooter

B Lageplan Vorentwurf mit Sparten

- 2.01-B-Sparten - Variante mit Autoscooter
- 2.10-A-Sparten - Variante ohne Autoscooter

C Kostenschätzung

D Voruntersuchung zur Verkehrsplanung / Kreuzung (6 Anlagen)

1. Lage und heutige Situation

Das Plangebiet befindet sich im Süden des Erlanger Stadtgebietes im Ortsteil Eltersdorf. Der Ortsteil umfasst heute rund 3.500 Einwohner. Der 1972 eingemeindete Ortsteil schließt südlich an den Stadtteil Bruck an und liegt im Spannungsfeld zwischen der Bundesautobahn A3 (Ost-West-Richtung), als auch der Bundesautobahn A73 und der Bahntrasse Nürnberg-Bamberg (beide Nord-Süd-Richtung). Diese Hauptverkehrswege führen direkt durch den Ortsteil und zum Teil nur wenige Meter neben der bestehenden Bebauung entlang. Östlich und südlich angrenzende Gewerbegebiete belasten den Ortsteil zusätzlich durch ein hohes Verkehrsaufkommen, zunehmend auch mit Schwerlastverkehr.

Der neu zu gestaltende Egidienplatz liegt mittig im Ortskern und wird durch die verkehrliche Situation dominiert: Hier trifft die Weinstraße aus dem Osten kommend auf die Eltersdorfer Straße in Nord-Süd-Richtung. Um den Egidienplatz befinden sich mehrere denkmalgeschützte Wohnhäuser sowie die Egidienkirche mit ihrem mittelalterlichen Chorturm. Im Süden des Platzes fließt in Ost-West-Richtung der Eltersdorfer Bach, der sogenannte „Hutgraben“. Der Platz selbst wird heute hauptsächlich als Parkplatz benutzt.

2022 wurde die Neubebauung, eine Filiale der Firma „Der Beck“, am Platz fertiggestellt und ist seitdem in Betrieb. Die öffentlichen Platzflächen grenzen an der westlichen Fassade des Platzes direkt ans Gebäude.

2. Verkehrliche Einbindung

Die Eltersdorfer Straße ist eine Staatsstraße und führt als Hauptverkehrsstraße in Nord-Süd-Richtung durch den Ortsteil. Die Weinstraße ist eine vom östlich gelegenen Tennenlohe kommende Kreisstraße, welche am Egidienplatz auf die Eltersdorfer Straße trifft. Beide Straßen liegen hier in der Baulast der Stadt Erlangen. Aktuell stellt der Egidienplatz einen Verkehrsknotenpunkt mit sehr hohem Verkehrsaufkommen dar. Eine Verkehrszählung aus dem Jahre 2015 ergab im Kreuzungsbereich ein Verkehrsaufkommen von bis zu 15.000 Fahrzeugen pro Tag. Lastwagen, Busse, PKW und landwirtschaftliche Fahrzeuge kreuzen sich am Egidienplatz in drei Richtungen. Die Buslinie 294 führt von Erlangen Zentrum über die Eltersdorfer Straße und den Egidienplatz ins südliche Eltersdorf und auch über die Weinstraße zum Bahnhof Eltersdorf und ins Gewerbegebiet „Am Pestalozziring“ und wieder zurück. Die Staatsstraße verbindet hier nicht nur das südliche Erlangen mit Fürth, südlich von Eltersdorf befindet sich auch eine Autobahnauffahrt auf die A73 in Richtung Nürnberg/Fürth bzw. Bamberg. Im Osten von Eltersdorf befindet sich ein Gewerbegebiet in dem sich aktuell unter anderem auch Logistikbetriebe befinden.

3. Abwägung Kreisverkehr oder T-Kreuzung

Im Zuge der Planung für die Umgestaltung des Egidienplatzes Eltersdorf wurden verschiedene Möglichkeiten geprüft, die Kreuzungssituation zu gestalten. Hierbei hat sich der Kreisverkehr als Vorzugsvariante herausgestellt. Kreisverkehre sind bei den Bürgerinnen und Bürgern generell sehr beliebt und werden auch in Erlangen an vielen Stellen immer wieder gefordert. Am Egidienplatz ist die Errichtung eines Mini-Kreisverkehrs erfreulicherweise möglich.

Nachdem die Ortsumfahrung Eltersdorf nicht wie geplant realisiert werden kann, stellt der Egidienplatz einen wichtigen Knotenpunkt im bestehenden Verkehrssystem in Eltersdorf dar. Der Ortsteil leidet unter einem hohen Maß an Durchgangsverkehr. Die Eltersdorfer Straße ist hierbei nicht nur die Nord-Süd-Verbindung zwischen Erlangen / Erlangen-Bruck in Richtung Stadeln und Fürth, sondern dient auch als Zubringer zu der im Süden befindlichen Auffahrt auf die A73. Analysen ergaben, dass es, um die vorhandenen Verkehrszahlen vor allem von auswärtigen bzw. durchfahrenden Fahrzeugen zu reduzieren, nötig ist, die Ortsdurchfahrt langsamer und unattraktiver zu gestalten. Als Knotenpunkt zwischen der

Weinstraße aus dem durch das Gewerbegebiet geprägten Osten und der in Nord-Süd-Richtung verlaufenden Eltersdorfer Straße, muss der Egidienplatz hierbei zwingend eine entscheidende verkehrsberuhigende bzw. steuernde Aufgabe erfüllen. Als Kreisverkehr ausgestaltet übt der Egidienplatz eine geschwindigkeitsdämpfende Wirkung auf den Verkehr in alle Fahrtrichtungen aus.

Ein Beibehalten der derzeitigen T-Kreuzung hätte zur Folge, dass der Verkehr auf der Eltersdorfer Straße weiterhin vorfahrtsberechtigt wäre und ein zügiges Durchfahren eher noch befördert würde. Da eine Geschwindigkeitsbeschränkung auf Tempo 30 im Bereich der Eltersdorfer Straße auf Grundlage der aktuell gültigen StVO in absehbarer Zeit nicht in Aussicht gestellt werden kann, ist dies eine Möglichkeit die Geschwindigkeit effektiv zu reduzieren und gleichzeitig den Verkehrsfluss aufrecht zu erhalten. Der Mini-Kreisverkehr ist ausreichend leistungsfähig, wogegen eine Einmündung nicht mehr leistungsfähig ist. Die derzeitige Einmündungssituation am Egidienplatz hat in den vergangenen Jahren zu einer Häufung von Unfällen geführt. Mit einem Mini-Kreisverkehr an dieser Stelle wird die Verkehrssicherheit deutlich erhöht. Außerdem bietet der Mini-Kreisverkehr zu Fuß Gehenden mehr sichere Querungsstellen in Form von Inseln als bei einer Einmündung möglich wären.

Aufgrund der eingeschränkten Fläche – der Egidienplatz soll entsprechend der Beschlussvorlage 611/033/2021 auch zu einem zentralen Dorfplatz mit Aufenthaltsqualität umgestaltet werden, wurde ein Durchmesser von 19m angeordnet, so dass es sich um einen Kreisverkehr mit überfahrbarer Mitte handeln muss. Busse, LKW und längere landwirtschaftliche Fahrzeuge können den gepflasterten Mittelkreis überfahren, was wiederum mit sich bringt, dass die Mitte nicht bepflanzt oder anderweitig gestaltet werden kann.

4. Besondere Anforderung Kerwa

Variante mit Autoscooter: Für die Anfang September stattfindende Stadteilkirchweih stellt der Egidienplatz und seine Umgebung einen Hauptbestandteil der für die Schausteller vorzusehenden Flächen dar. So soll weiterhin möglich sein, hier einen 16 x 33 Meter messenden Autoscooter aufstellen zu können. Dieser muss nach Rücksprache mit der Feuerwehr (Hr. Weidinger) mindestens 3 Meter von Gebäuden entfernt sein, so dass die entsprechenden Rettungswege gewährleistet werden können. Weiter ist auch die Eltersdorfer Straße soweit freizuhalten, dass Rettungsfahrzeuge und auch der Kirchweihumzug nicht behindert werden. Der vorliegende Vorentwurf 2.01 hat die Anforderungen des Autoscooters als Planungsgrundlage. Dementsprechend ist der zentrale Platzbereich freigehalten, insbesondere von Bäumen und Aufkantungen im Straßenbereich. Poller sind herausnehmbar, Querungsinseln sind reversibel.

Variante ohne Autoscooter: Nach Wunsch der Bürgerschaft vor Ort und der Stadt Erlangen wurde alternativ eine Platzgestaltung ohne Autoscooter entwickelt, Vorentwurf 2.10. Hier sind Baumpflanzungen, Pflanzbeete, feste Bänke sowie ein Brunnenelement möglich.

5. Variantenuntersuchung Verkehrsknotenpunkt Vertiefung (Oktober 2022)

A) Variante Kreisverkehr

Wie in Unterlage 5/1 dargestellt, wird die bestehende Linksabbiegespur und Querungsstelle rückgebaut. Bei dieser Variante wurde ein Kreisverkehr mit einem Durchmesser von 19,00 m angeordnet. Es wurden im Bereich der Eltersdorfer Straße zwei Querungen geplant. Da die südliche Querungsstelle für die Fußgänger eine wichtige Verbindung ist, wurde hier die größere Querung der Variante 2b (Stand 13.06.2022) übernommen. Im nördlichen Bereich wurde die Querung aus der Variante 2c (Stand 13.06.2022) übernommen. Diese ist schmaler ausgebildet. Die Insel im Bereich der Weinstraße wird

überfahrbar ausgebildet. Im nördlichen Bereich kann eine überfahrbare markierte Engstelle angeordnet werden, um den ankommenden Verkehr zu verlangsamen.

B) Variante Linksabbiegespur

Wie in Unterlage 5/2 Variante Linksabbiegespur dargestellt, setzt sich der Querschnitt aus je 3,50 m Fahrbahn und 3,00 m für Linksabbieger zusammen damit ergibt sich eine Gesamtbreite von 10,00 m.

C) Weinstraße

Die Weinstraße soll als „Tempo 20 - Verkehrsberuhigter Geschäftsbereich“ ausgebildet werden. Um dies optisch darzustellen, wird die Fahrbahnfläche gepflastert. Der Gehweg wird ebenfalls gepflastert und mit Borden von der Fahrbahn abgehoben. Im Bereich der Hausnummer 7 wurde eine Engstelle mit einer Durchfahrtsbreite von 4,0 m angeordnet. Diese bewirkt eine Geschwindigkeitsreduzierung der aus Osten kommenden Fahrzeuge, die in den Egidienplatz einfahren.

6. Gehölzbestand, Neupflanzung und Grünflächen.

Auf Höhe des Egidienplatzes befinden sich mehrere Bäume im Uferbereich des Baches, die unter die Baumschutzverordnung der Stadt Erlangen fallen. Hierbei handelt es sich um zwei Erlen, eine Edelkastanie und mehrere Weiden. Da die Bäume auf der Südseite des Baches liegen, sind sie von der Planung weitgehend unberührt. Auf der Nordseite werden im Bereich des renaturierten Uferbereiches neue Bäume (Auengehölze des Überflutungsbereiches) vorgesehen. Die Bepflanzung des Uferbereiches erfolgt über geeignete Stauden. Falls technisch erforderlich erfolgt hier eine Böschungsbefestigung.

Im Bereich des öffentlichen Gehweges auf Höhe des Egidienplatz Nr. 1 sind zwei große Linden vorzufinden, die im Rahmen der Neuplanung integriert und mit neuen Baumscheiben versehen werden. Nördlich hiervon wird ein weiterer Baum im Gehweg ergänzt. Weiterhin werden östlich des Kreisverkehrs 3 Baumquartiere und in der Weinstraße im Bereich der Fahrbahnverengung 1 Baumquartier vorgesehen.

Variante ohne Autoscooter: In der alternativen Planung ohne Autoscooter werden zusätzlich zu den vorbeschriebenen Neupflanzungen 5 Laubbäume erster Ordnung (gemischt / klimatolerant) straßenbegleitend auf dem Platz vorgeschlagen. Diese stehen in offenen, bepflanzten (pflegearme Staudenmischung) Baumscheiben.

7. Renaturierung des Eltersdorfer Baches / Überflutung

Der Eltersdorfer Bach soll im Bereich des Egidienplatzes geöffnet und erlebbar gemacht werden. Durch den Abbruch der bestehenden Beton-Ufermauer am Nordufer des Baches wird die Grundlage für einen geböschten und grünen Uferbereich geschaffen. Der Retentionsraum des Baches kann so wesentlich vergrößert werden und der Zugang zum Wasser über eine Freitreppe realisiert werden. Einzelne Sitzblöcke in der Treppe ermöglichen dort das Sitzen am Bachufer. Die Höhenlagen des HQ100 wurden berücksichtigt, ebenso wie eine Stützmauer zur Sicherung der Böschungsoberkante am „Beck“. Im Rahmen der LPH 4 wird ein wasserrechtliches Genehmigungsverfahren notwendig.

8. Materialkonzept: Einbauten und Ausstattung

Variante mit Autoscooter: Im Bereich des Egidienplatzes erfolgen aufgrund des Autoscooters größtenteils keine festen Einbauten. Entlang der Eltersdorfer Straße, sowie entlang der Weinstraße werden am Platzrand Absperrpfosten (je nach Anforderung in herausnehmbarer oder ortsfester Ausführung)

angeordnet, um Wildparken zu verhindern. Für die temporäre Aufstellung des Weihnachtsbaumes ist eine Bodenhülse in das Pflaster integriert. Die Straßenbeleuchtung wird wo notwendig versetzt.

Variante ohne Autoscooter: In der alternativen Planung ohne Autoscooter werden an der östlichen Seite der grünen Baumscheiben feste Bänke mit Lehne eingeplant (Holz-Stahl-Konstruktion). Als zentrales Element ist ein kleines Brunnenelement in der Platzmitte vorgesehen. Für die temporäre Aufstellung des Weihnachtsbaumes ist eine Bodenhülse in das Pflaster integriert. Die Straßenbeleuchtung wird wo notwendig versetzt, vereinzelt werden notwendige Absperrpfosten (je nach Anforderung in herausnehmbarer oder ortsfester Ausführung), als Schutz vor Wildparken oder Überfahren des Platzes gesetzt.


9. Materialkonzept: Oberflächen


Um der Dorfmitte auch in der Oberflächengestaltung eine Wertigkeit zu geben, wird vorgeschlagen die Nebenflächen (Gehwege) sowie den Egidienplatz in Naturstein (heimischen Granit) zu belegen. Zusätzlich wird die Weinstraße zur Verkehrsberuhigung ebenfalls gepflastert. Im Detail wird ein Pflasterteppich aus ungebundenem, gesägtem Großpflaster Granit (16x16 cm) für die eben genannten Bereiche geplant. Auf dem Egidienplatz sind zudem Granit-Platten (32x64 cm) eingestreut. Letztere geben zusätzlich eine Orientierung in Richtung der Treppenanlage am Bach. Alle Flächen sind Schwerlastbefahrbar.

Die Straßenflächen der Eltersdorfer Straße sind in regulärem Asphaltausbau vorgesehen.

Aufgestellt:

Nürnberg, 02.08.2023 – War/Vo

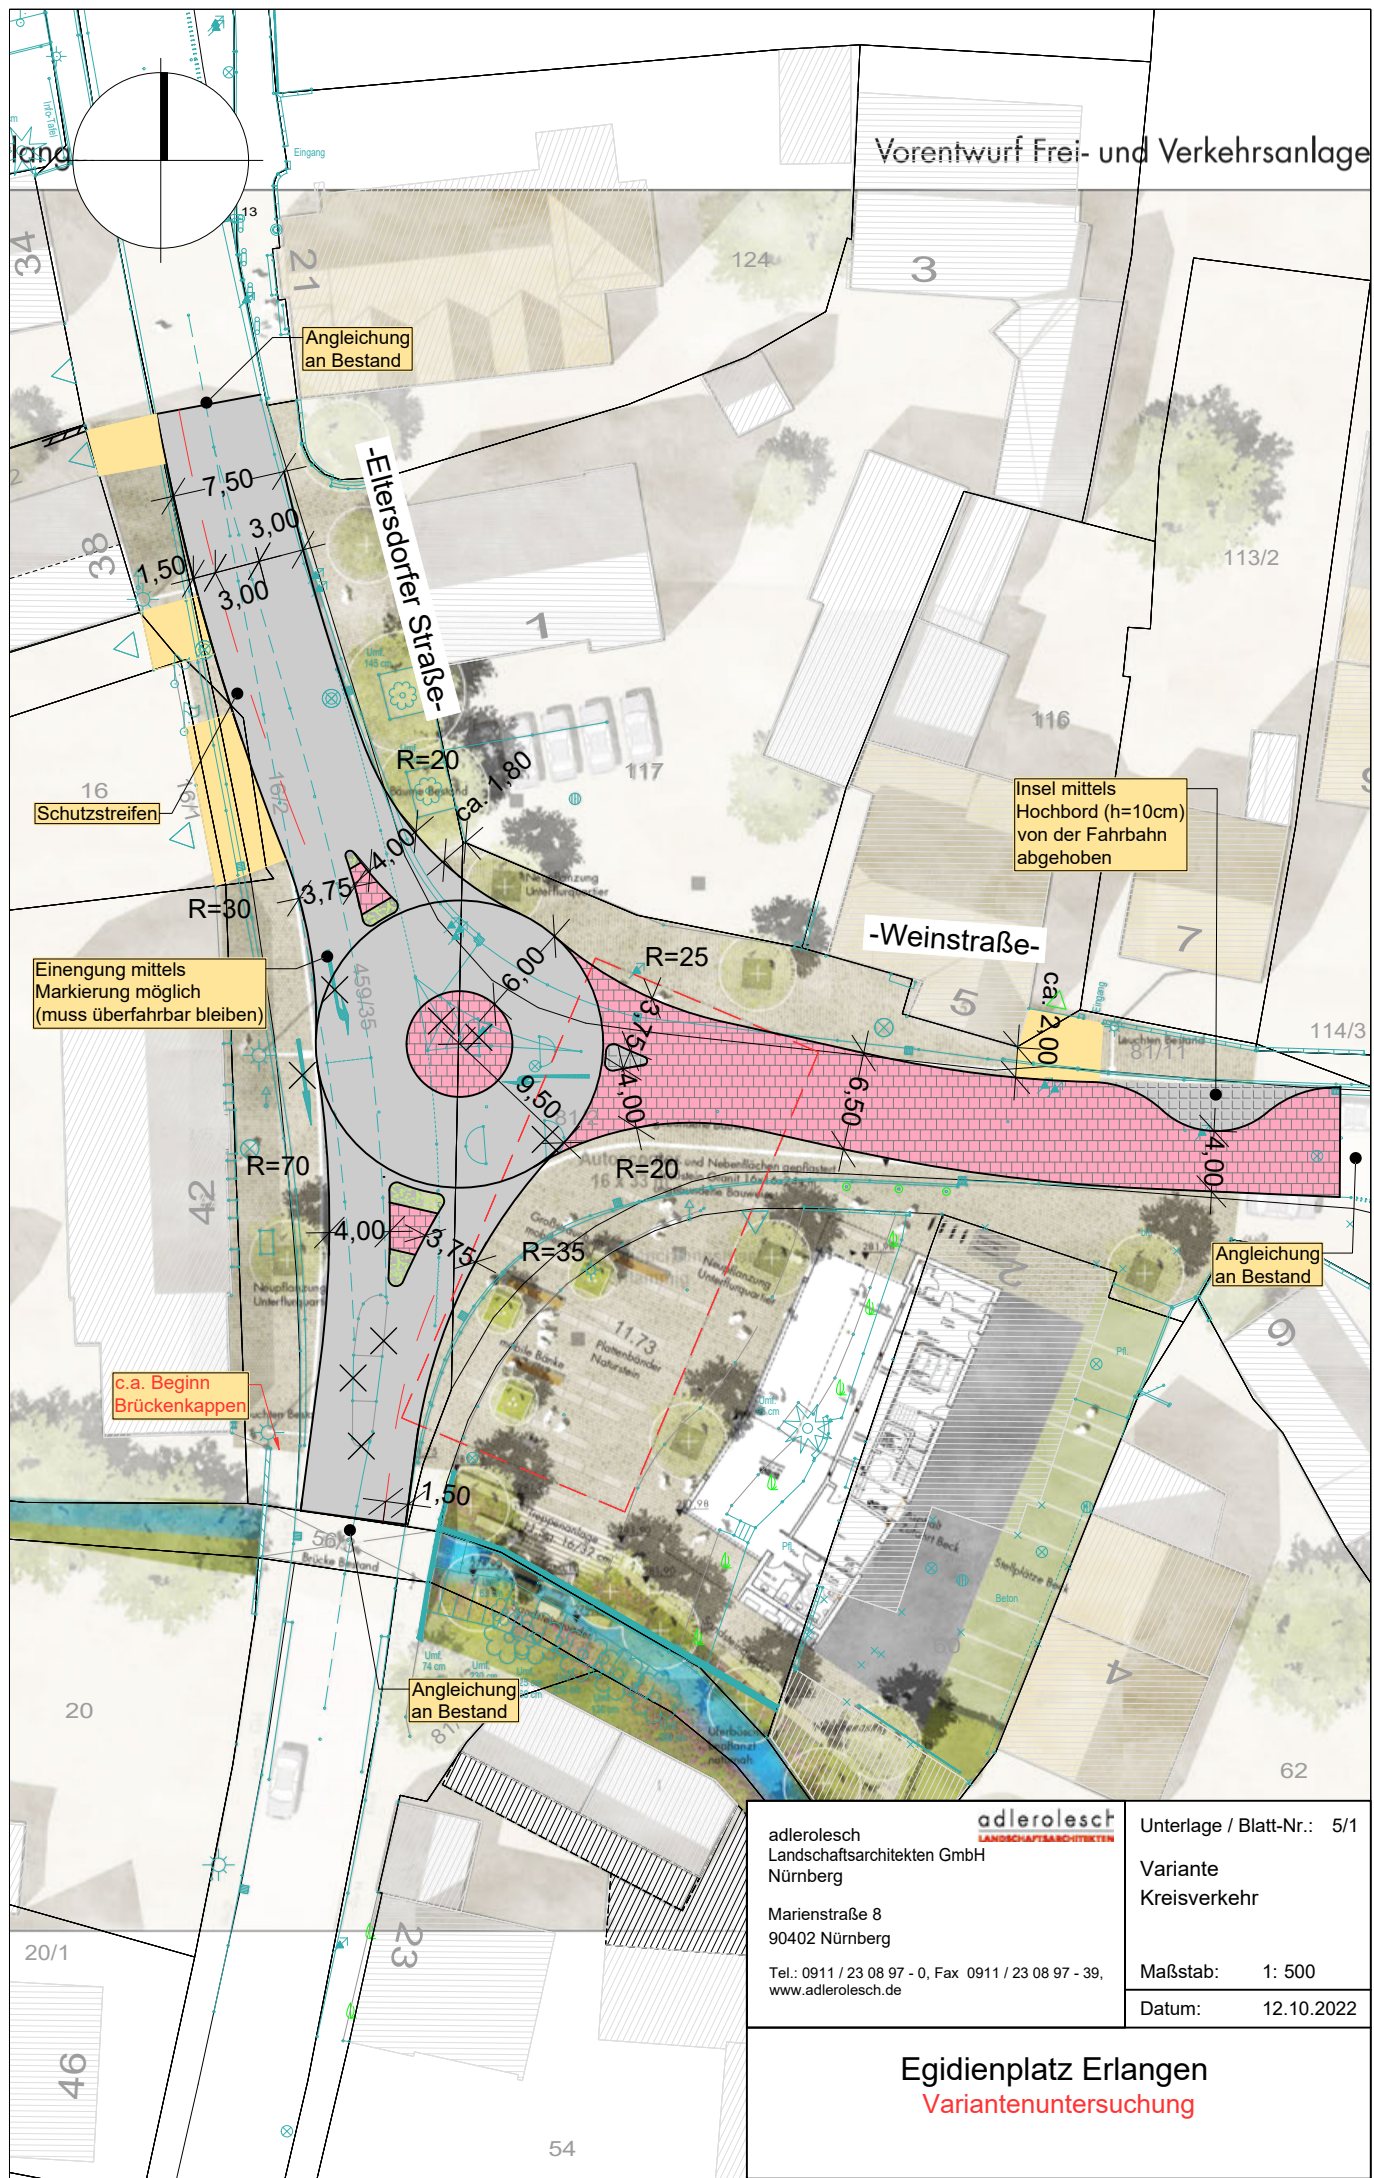

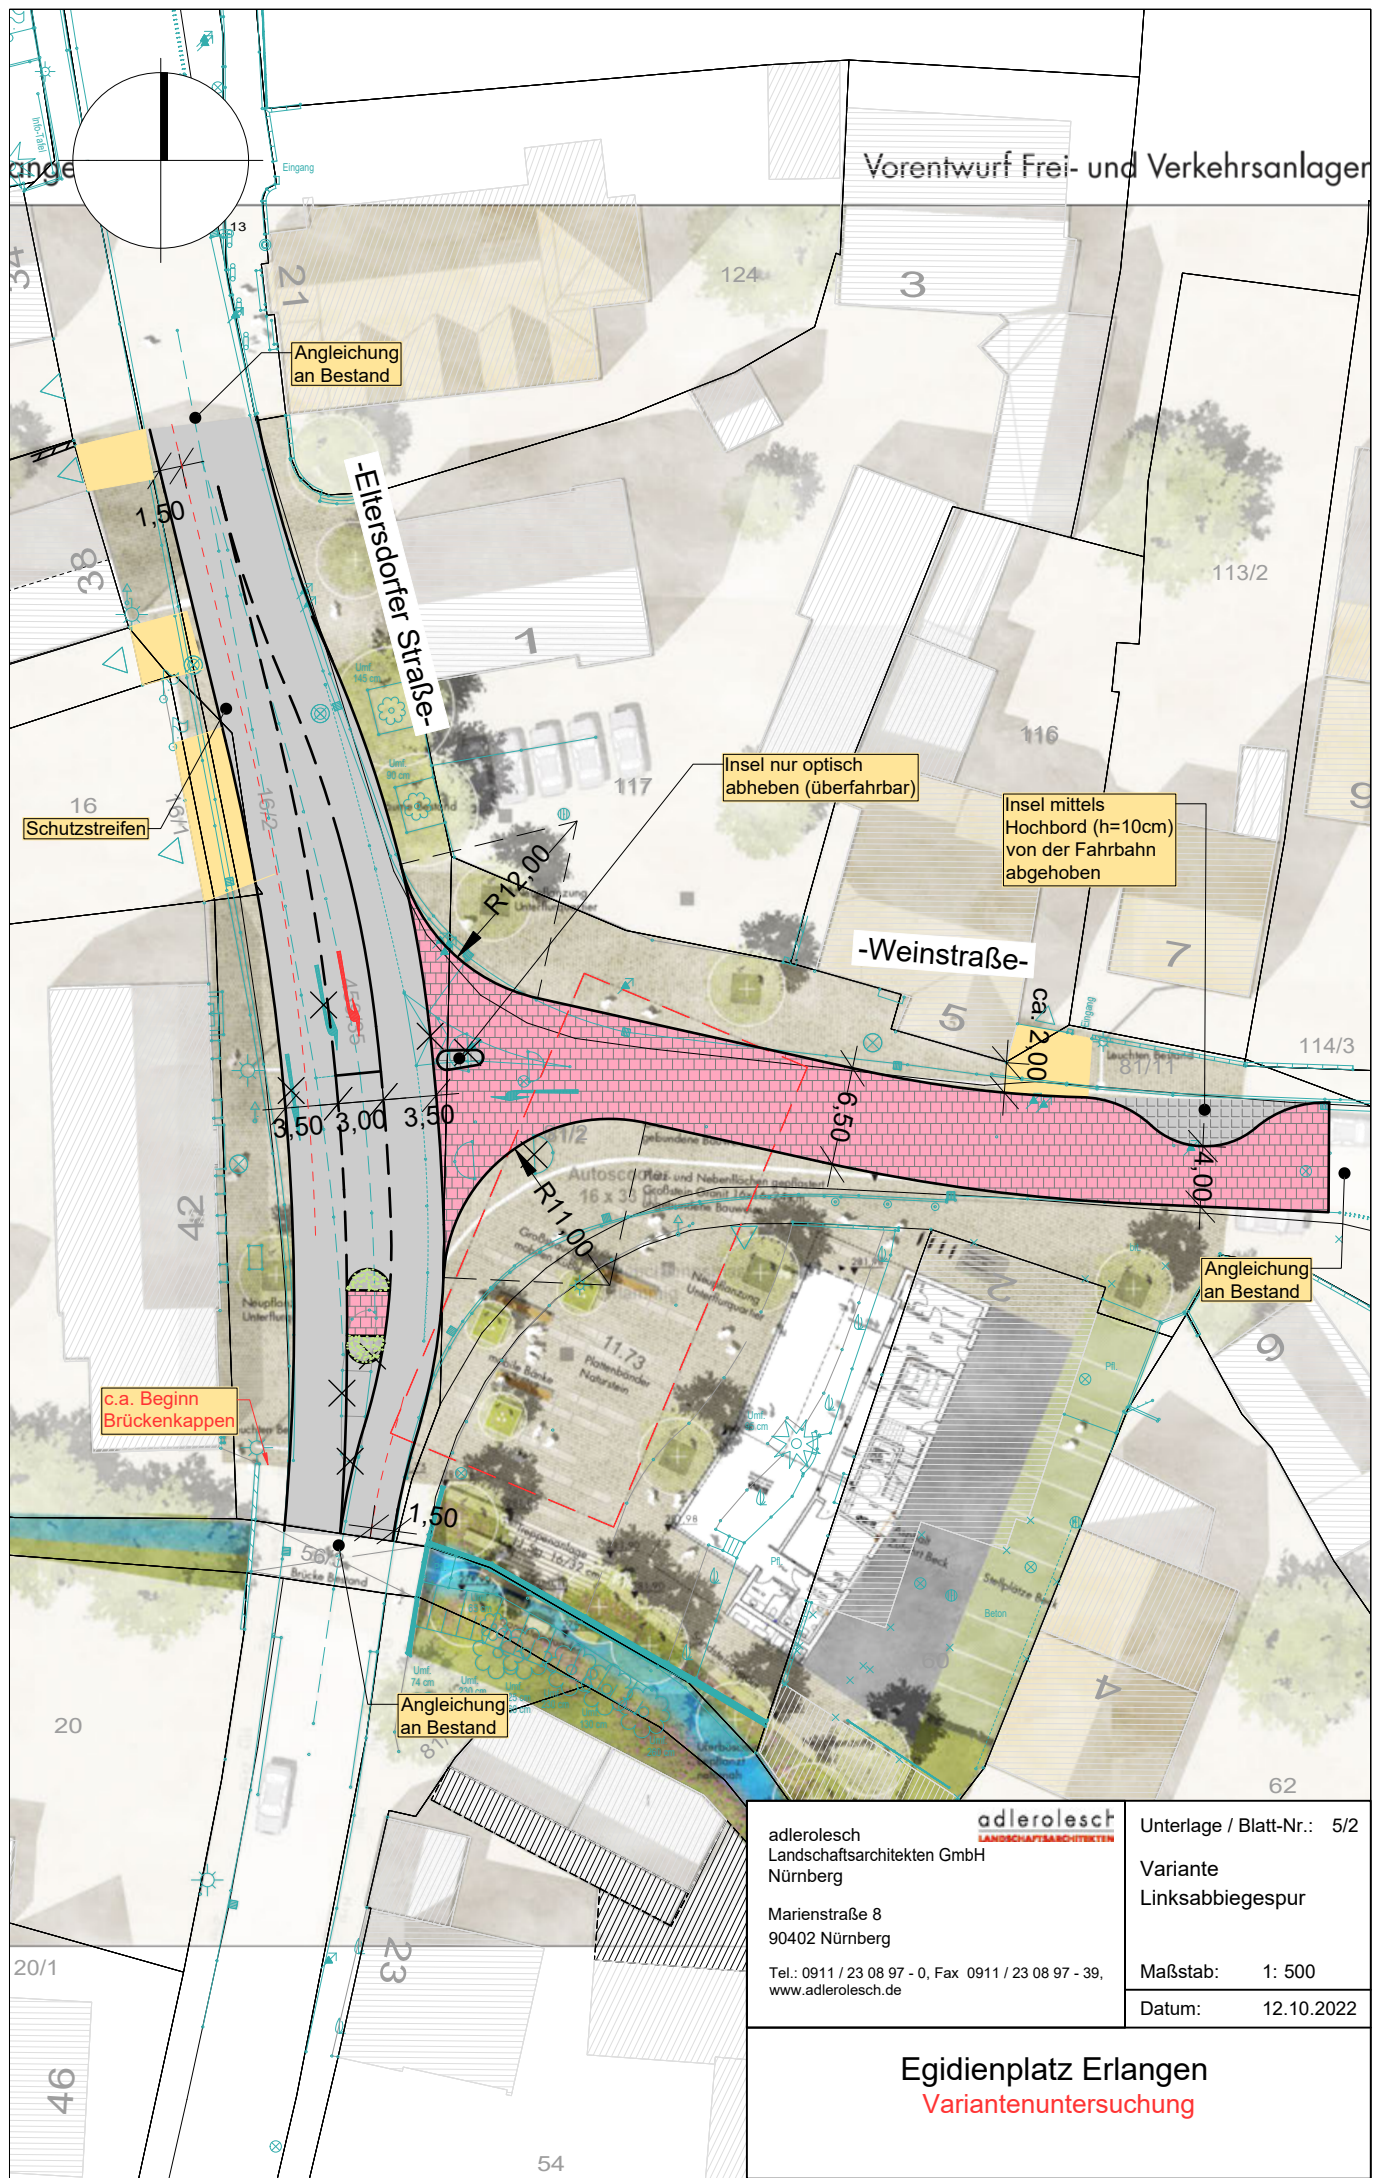

adlerolesch
Landschaftsarchitekten GmbH
Nürnberg
Marienstraße 8
90402 Nürnberg
Tel.: 0911 / 23 08 97 - 0, Fax 0911 / 23 08 97 - 39,
www.adlerolesch.de

Unterlage / Blatt-Nr.: 5/2
Variante
Linksabbiegespur
Maßstab: 1: 500
Datum: 12.10.2022

Egidienplatz Erlangen
Variantenuntersuchung