



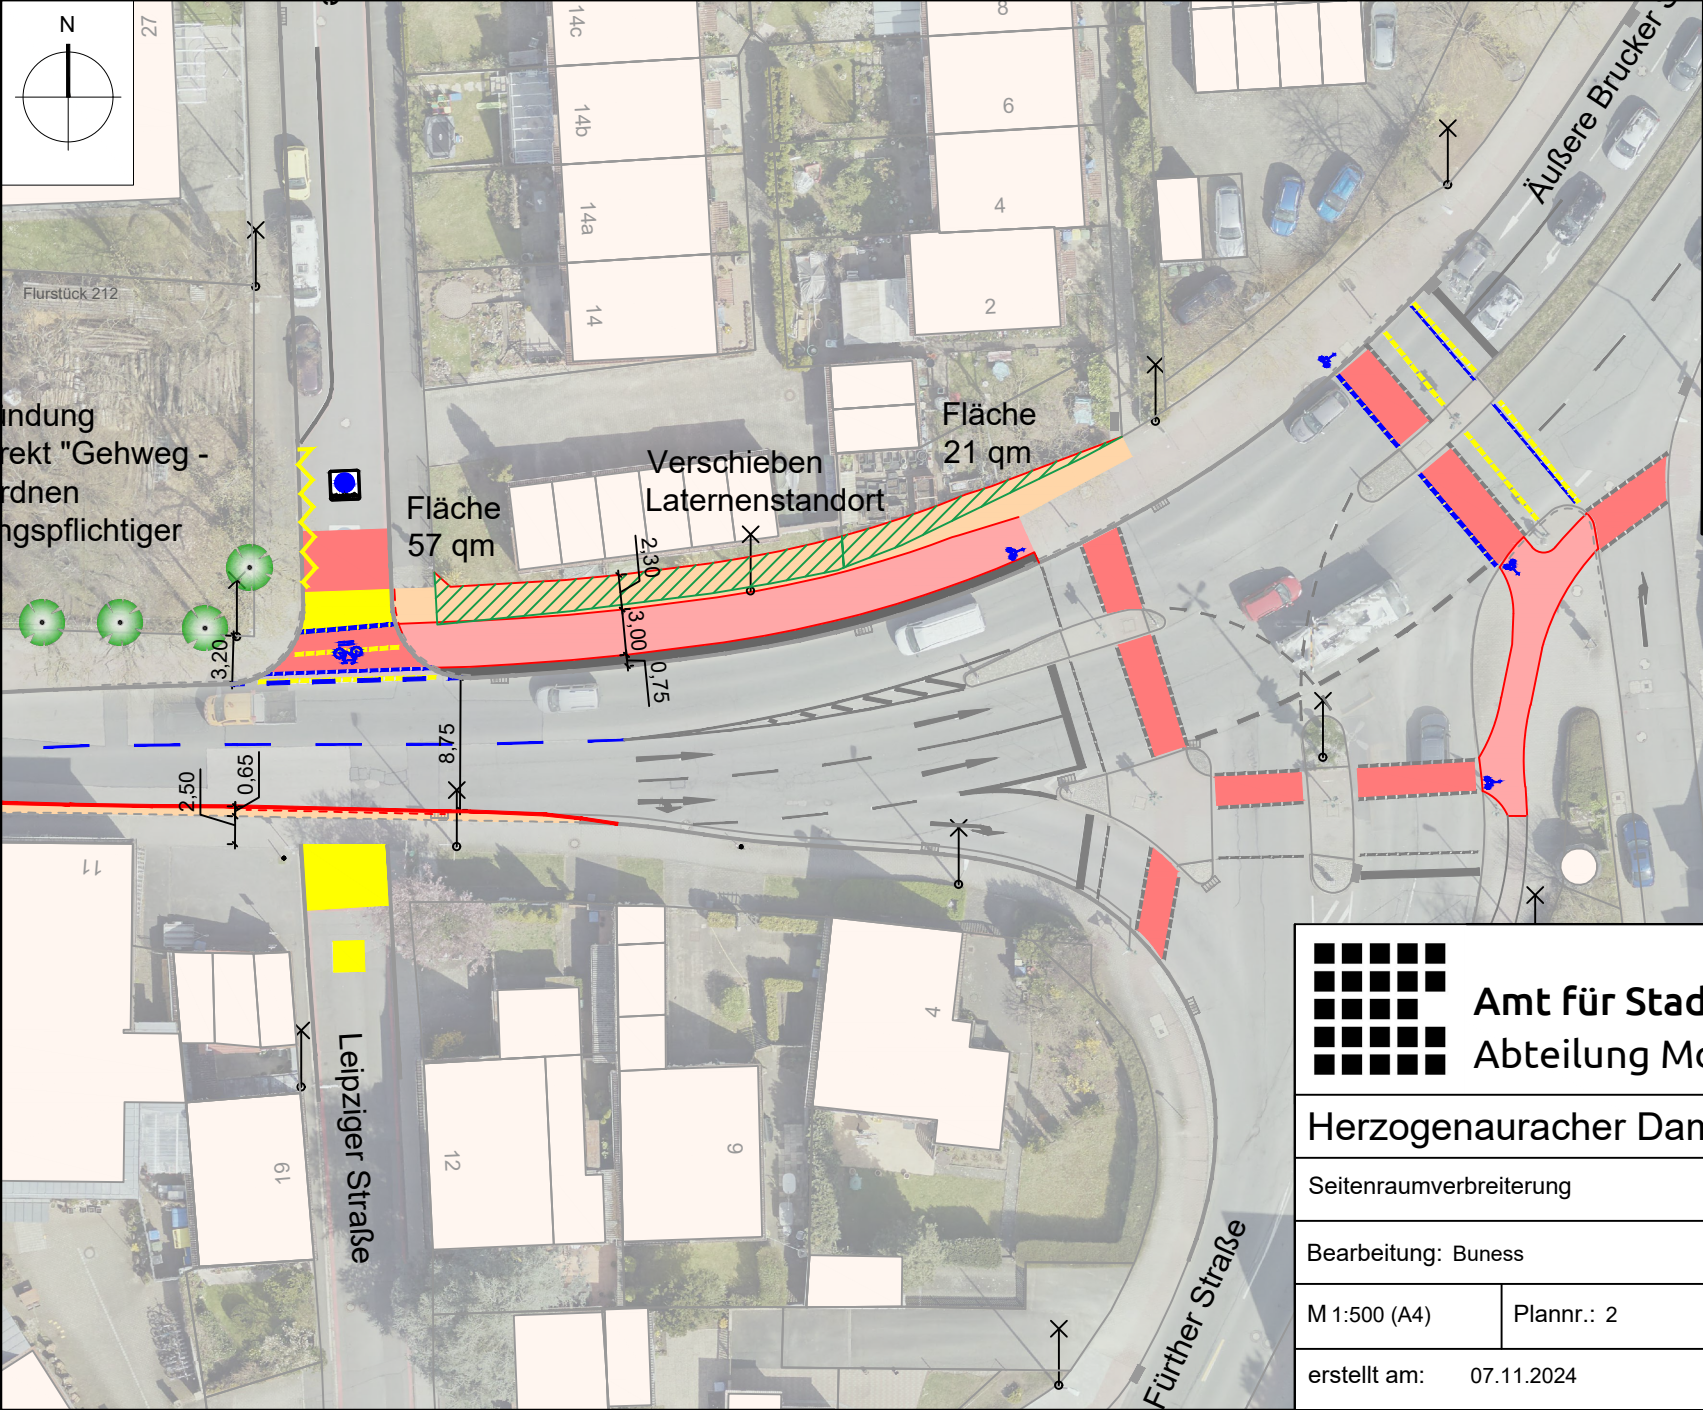

**Legende**

- Gehweg
- Bordsteinradweg
- Parkstreifen / Insel / Fahrbahnteiler
- Grünfläche
- Roteinfärbung Asphalt (Radweg)
- Gebäude
- Bordstein/ abgesenkt
- Bestand
- Planung
- Abbruch
- Markierung Neu
- Markierung entfernen
- bestehender Baum
- Grunderwerb

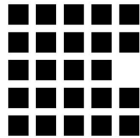

**Amt für Stadtplanung und Mobilität**  
**Abteilung Mobilitätsplanung**

**Herzogenauracher Damm**

Seitenraumverbreiterung

|                         |            |                           |
|-------------------------|------------|---------------------------|
| Bearbeitung: Bunes      |            | SG.-Leitung: gez. Reußner |
| M 1:500 (A4)            | Plannr.: 2 | Abt.-Leitung: gez. Korda  |
| erstellt am: 07.11.2024 |            | Amtsleitung: gez. Lohse   |